PLANILLA DE UNIDADES FUNCIONALES

Unidad Func.	Piso	Cubierta m²	Semicub m²	Descub m²	Balcon m²	Total por piso m²	Total por unidad m²	Porcentual fiscal %	Observaciones
1	PB	26.28	—	3.75	—	30.03	30.03	4.52	
2	1°	54.66	—	—	—	54.66	54.66	9.19	
3	1°	34.54	—	—	—	34.54	34.54	5.81	
4	1°	52.74	—	—	—	52.74	52.74	8.87	
5	2°	54.66	—	—	—	54.66	54.66	9.19	
6	2°	34.54	—	—	—	34.54	34.54	5.81	
7	2°	52.74	—	—	—	52.74	52.74	8.87	
8	3°	54.66	—	—	—	54.66	54.66	9.19	
9	3°	34.54	—	—	—	34.54	34.54	5.81	
10	3°	52.74	—	—	—	52.74	52.74	8.87	
11	4°	54.66	—	—	—	54.66	54.66	9.19	
12	4°	34.54	—	—	—	34.54	34.54	5.81	
13	4°	52.74	—	—	—	52.74	52.74	8.87	
TOTALES		594.04	—	3.75	—	597.79	597.79	100.00	

NOTA: Los porcentuales fiscales indicados en esta planilla han sido calculados por el profesional y la exactitud de los mismos, queda bajo su exclusiva responsabilidad.

PLANILLA DE SUPERFICIES COMUNES

Planta	Cubierta	Semicub	Descub	Balcon	Total	Observaciones
BAJA	213.46	2.87	34.30	—	250.63	
PISO 1°	36.85	—	—	—	36.85	
PISO 2°	36.85	—	—	—	36.85	
PISO 3°	36.85	—	—	—	36.85	
PISO 4°	36.85	—	—	—	36.85	
TOTALES	360.86	2.87	34.30	—	398.03	

DETALLE 1

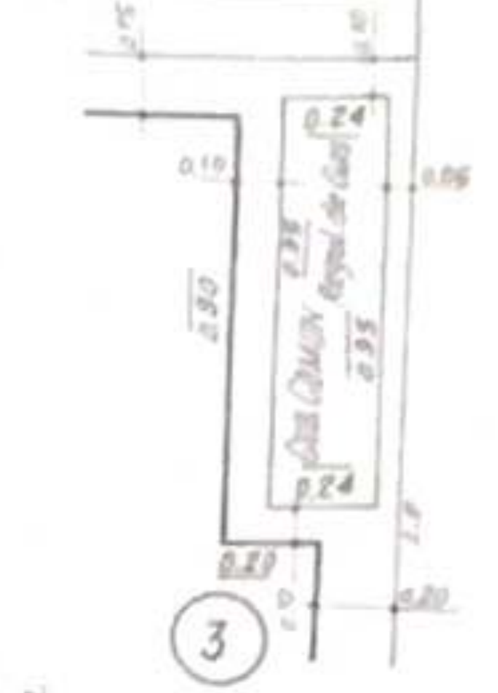

CROQUIS S/TITULO

NOTA: El titulo no consigna superficie

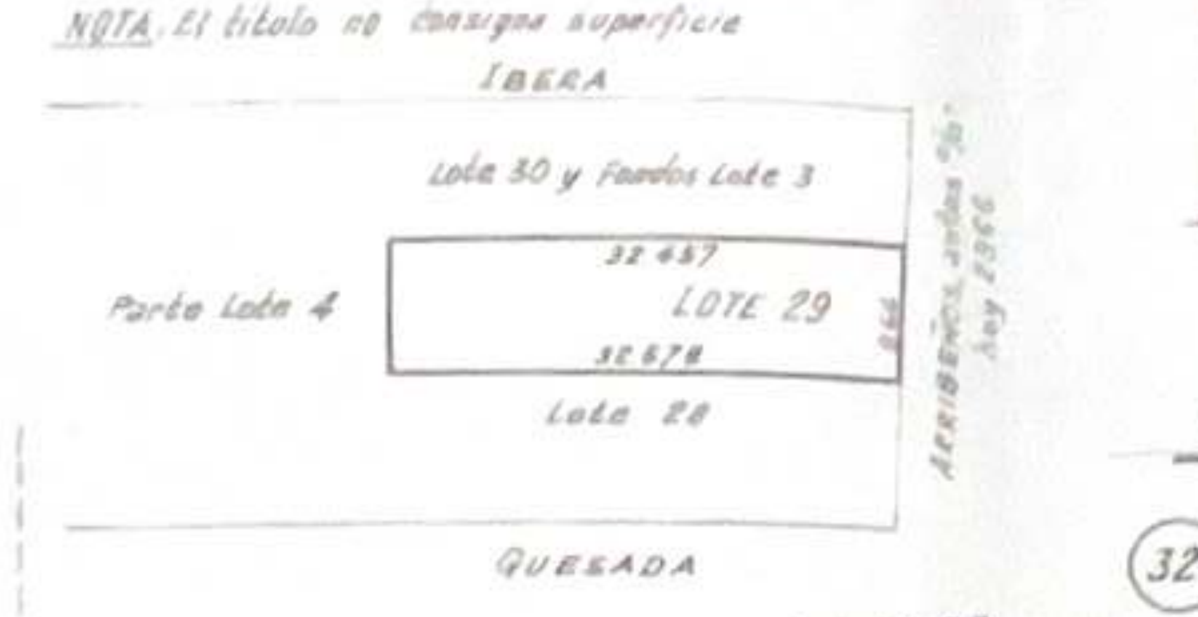

BALANCE DE SUPERFICIES

SUP S/MENSURA PARC 31	280,66 m²
SUP S/TITULO Lote 29 (calculada)	281,22 m²
DIFERENCIA EN MENOS	0,56 m²

PLANO SEGUN MENSURA

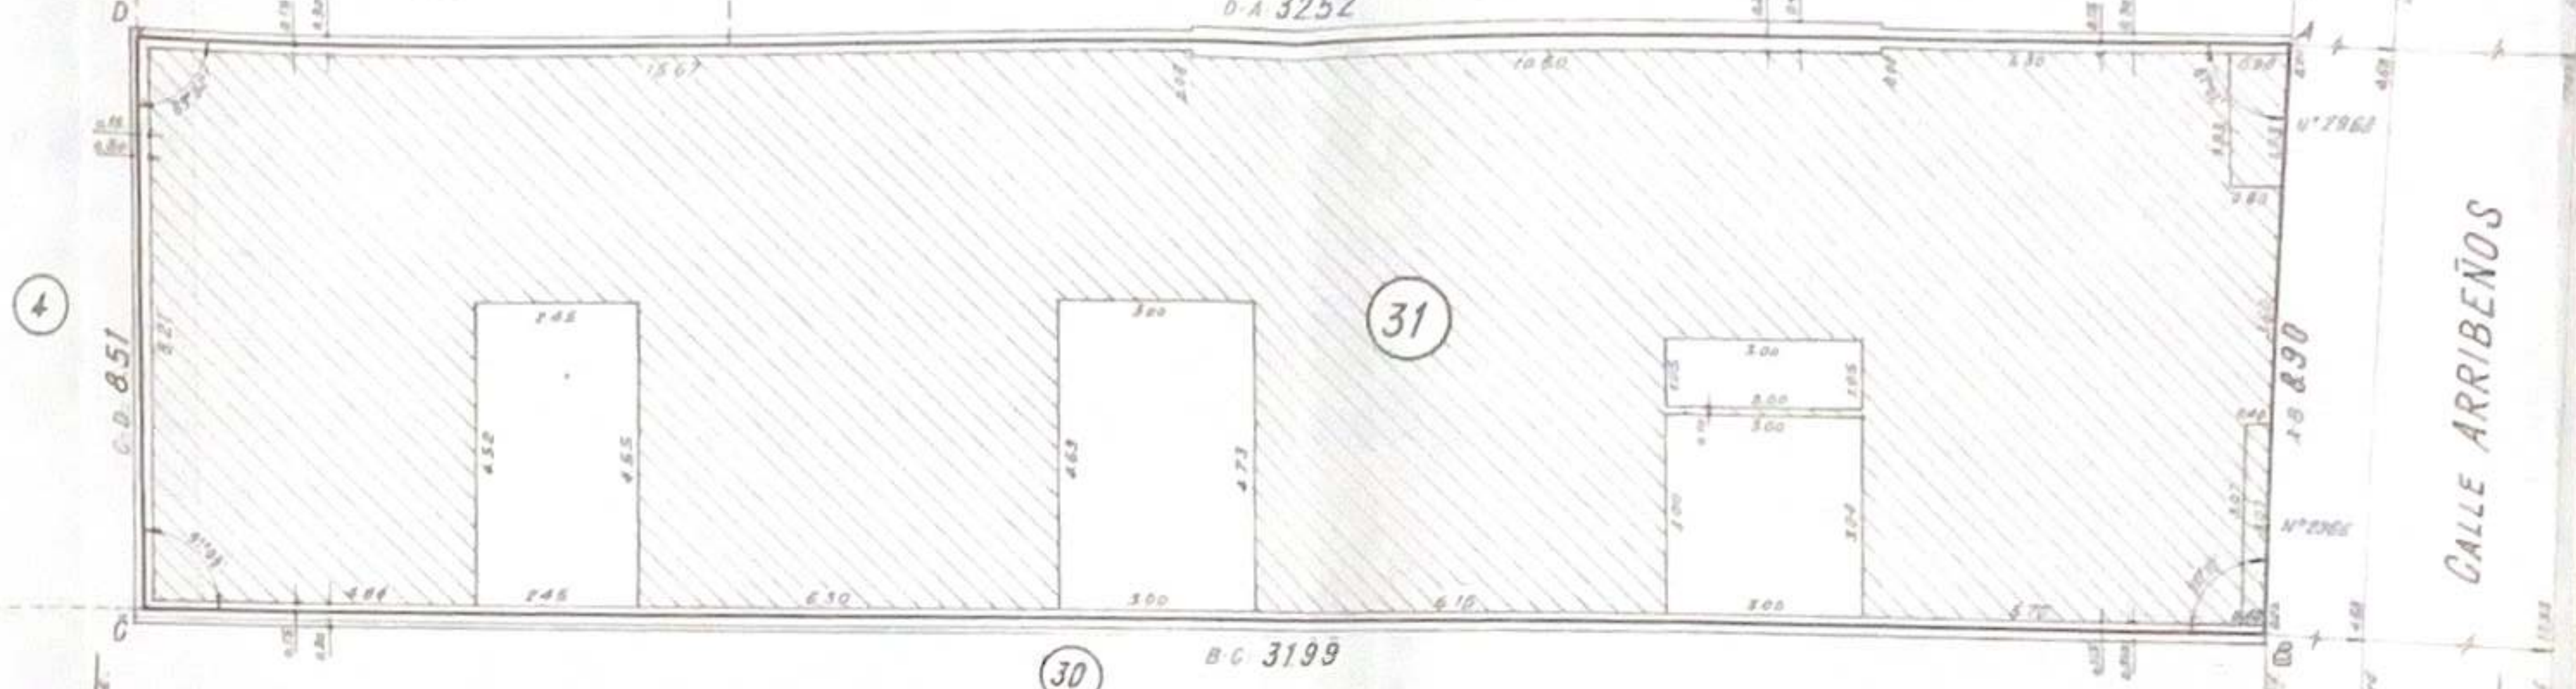

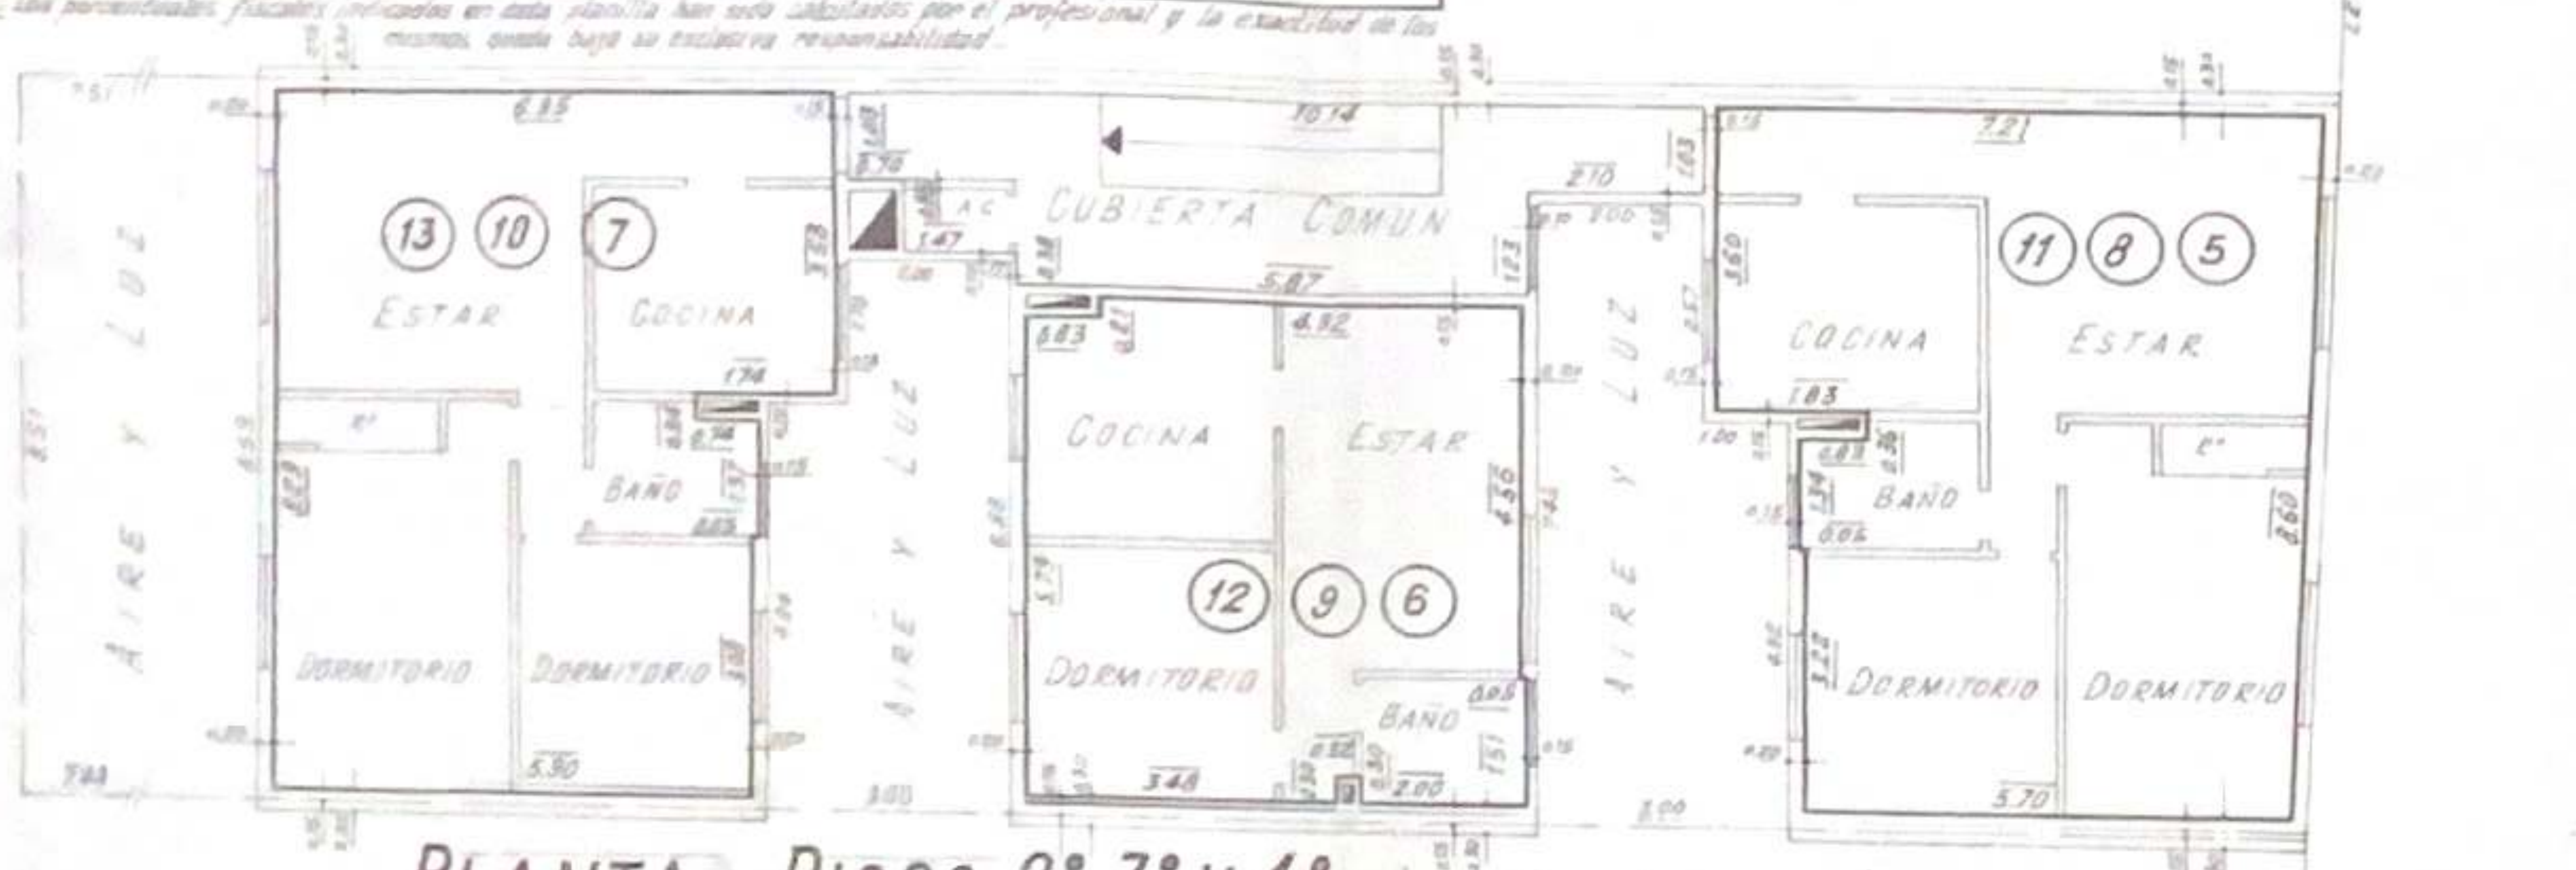

PLANTA PISOS 2°-3° Y 4° +6.10, +8.90, +11.70

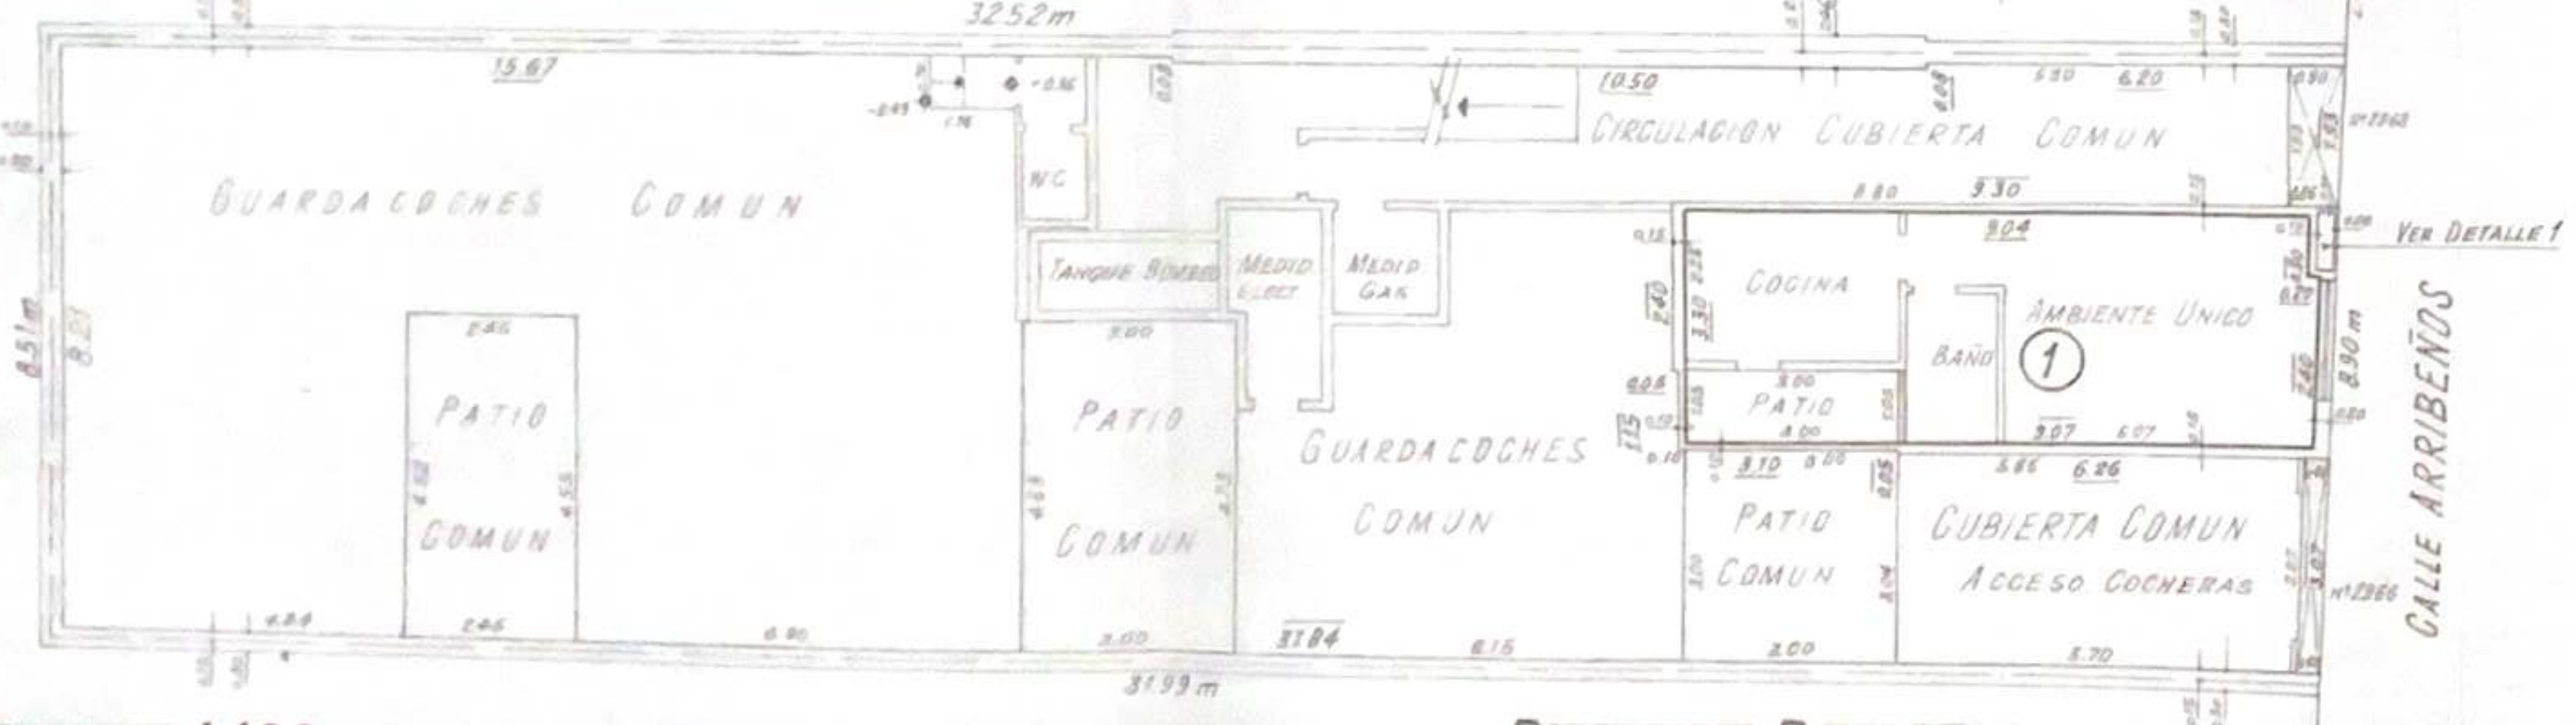

ESCALA 1:100 — NOTA: Todas las medidas lineales están expresadas en metros.

PLANTA BAJA +0.20

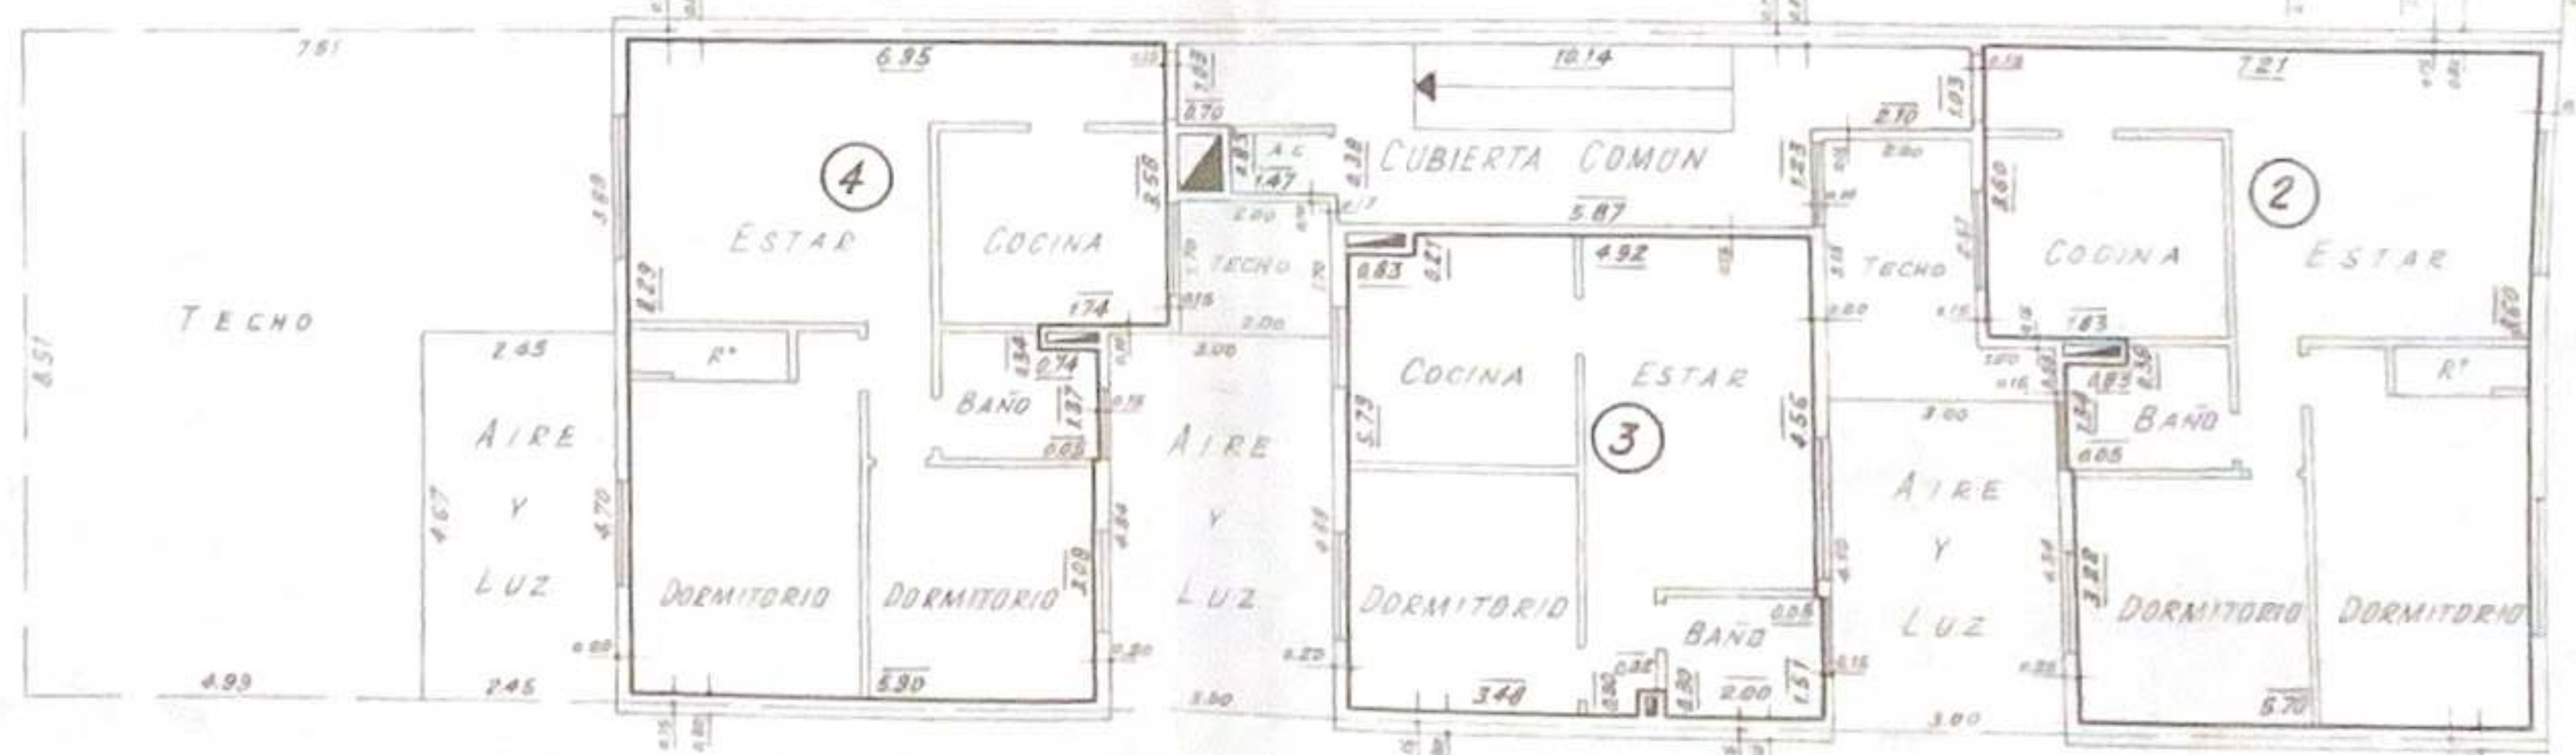

PLANTA PISO 1° +3.30

CARPETA N° 176343

CAPITAL FEDERAL

MENSURA PARTICULAR Y DIVISION POR EL REGIMEN DE PROPIEDAD HORIZONTAL - LEY 13.512 93

PARCELA 31 - MANZANA 72 - SECCION 27 - CIRCUNSCRIPCION 16

CALLE: ARRIBEÑOS N° 2966/68

PROPIETARIO:

JORGE MARSEILLAN Y CIA.

SOCIEDAD ANONIMA CONSTRUCTORA, INMOBILIARIA, FINANCIERA

PARTIDA DE ORIGEN: N° 337800

INSCRIPCION DE DOMINIO: MATRICULA 16-11951

CROQUIS DE LOCALIZACION

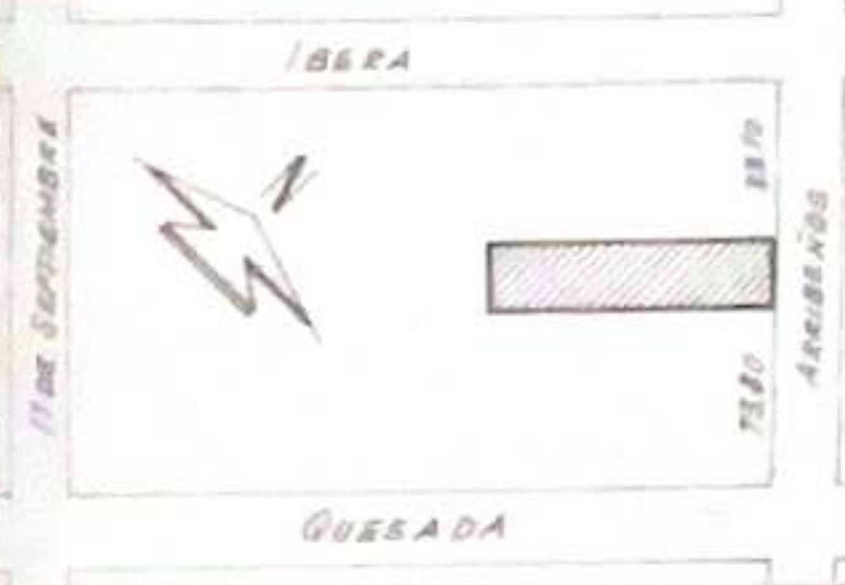

ZONIFICACION

HM5	R7	A4

PROPIETARIO

por Jorge Marseillan y Cia. S.A.C.I.F.

Rodolfo Juan Celia
Apoderado - LE 2784248

Domicilio Sarmiento 440 - Cap. Fed.

Del cotejo del presente plano con el de obra aprobado, efectuado por el profesional, surge que no existen construcciones realizadas sin permiso a la fecha de la mensura.
Se cumple con los Art. 1° y 2° de la Ley 13.512.

FECHA DE MENSURA: SEPT. /75

ALBERTO MANZORRO
AGRIMENSOR
Domicilio: Moreno 442 - 2° A - Cap. Federal
Inscrip. S. Obo. 17.946/44 - N° 1756
Inscrip. D. Catastro Munic.: N° 1270

REGISTRADO
EL REGISTRO DEL PRESENTE PLANO NO IMPLICA RECONOCER LAS LINEAS MUNICIPALES.-

13 NOV 1975

SANTIAGO KLEIMAN
AGRIMENSOR

M.H.-1843-75

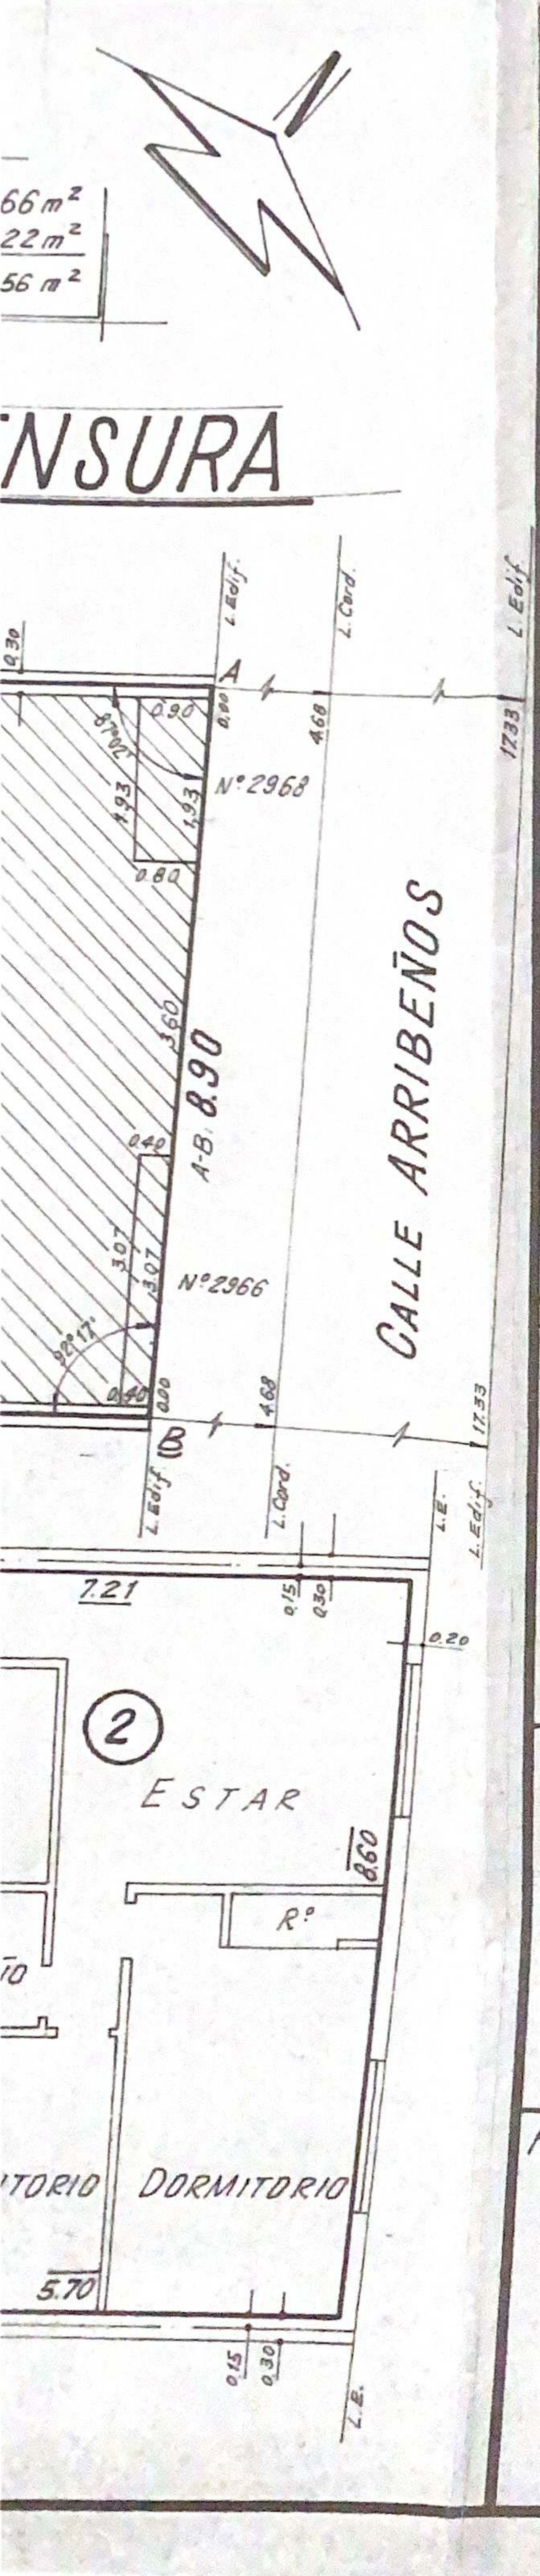

CARPETA Nº 176.349 D.G.F.O.T. /75

CAPITAL FEDERAL

MENSURA PARTICULAR Y DIVISION POR EL REGIMEN DE PROPIEDAD HORIZONTAL ~ LEY 13.512

93

PARCELA: 31 ~ MANZANA: 72 ~ SECCION: 27 ~ CIRCUNSCRIPCION: 16

CALLE: ARRIBEÑOS Nº 2966/68

PROPIETARIO:

JORGE MARSEILLAN Y CIA.

SOCIEDAD ANONIMA CONSTRUCTORA, INMOBILIARIA, FINANCIERA

PARTIDA DE ORIGEN: Nº 337.800

INSCRIPCION DE DOMINIO: MATRICULA 16-11.951

CROQUIS DE LOCALIZACION

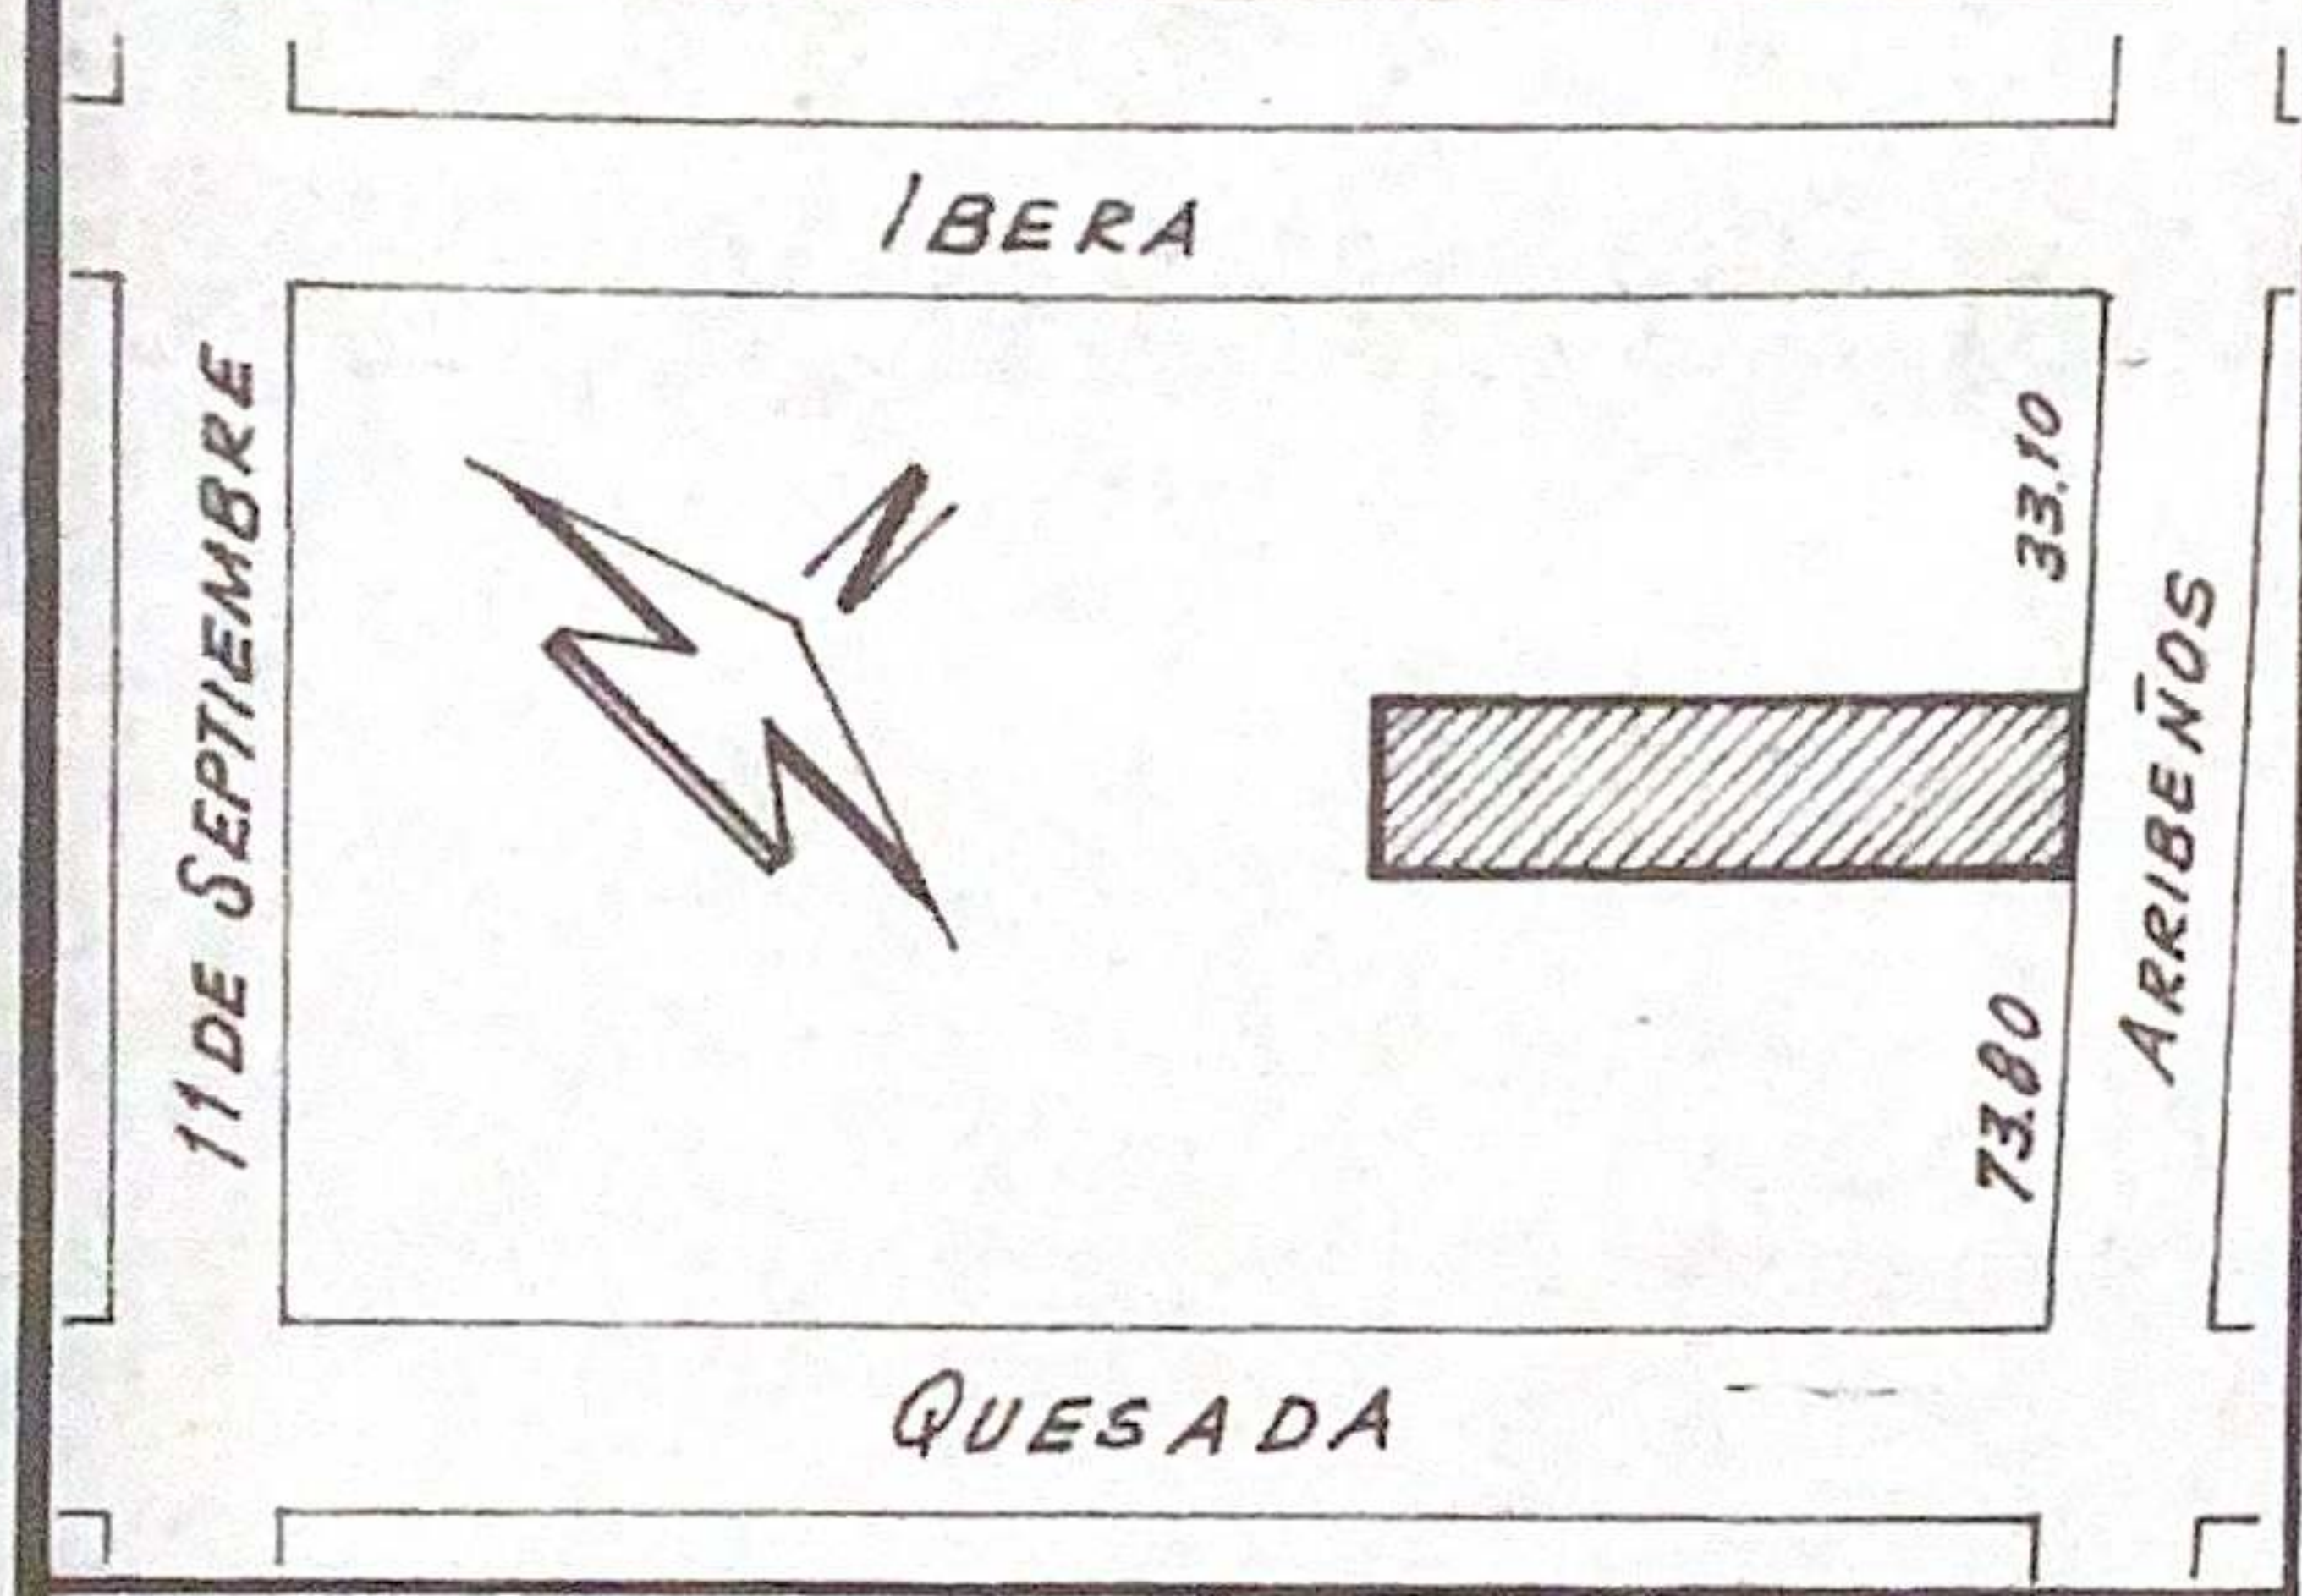

ZONIFICACION

HM5	R7	A4

PROPIETARIO:

por Jorge Marseillán y Cía. S.A.C.I.F.

Rodolfo Juan Celía
Apoderado ~ C.I. 2.784.248

Domicilio: Sarmiento 440 ~ Cap. Fed.

DEL COTEJO DEL PRESENTE PLANO CON EL DE OBRA APROBADO, EFECTUADO POR EL PROFESIONAL, SURGE QUE NO EXISTEN CONSTRUCCIONES REALIZADAS SIN PERMISO A LA FECHA DE LA MENSURA.-

SE CUMPLE CON LOS ART. 1º Y 2º DE LA LEY 13.512.-

REGISTRADO

EL REGISTRO DEL PRESENTE PLANO NO IMPLICA RECONOCER LAS LINEAS MUNICIPALES.-

13 NOV 1975

SANTIAGO KLEIMAN
AGRIMENSOR
JEFE DIVISION MENSURAS Y
DIRECCION DE CATASTRO

FECHA DE MENSURA: SEPT. /75

ALBERTO MANZORRO
AGRIMENSOR
DOMICILIO: MORENO 442-2º A - CAP. FEDERAL
INSCRIP. S. Dto. 17.946/44: Nº 1756
INSCRIP. D. CATASTRO MUNIC.: Nº 1370

M.H.-1843-75